LEGEND

LOD	LIMIT OF DISTURBANCE
SF	SILT FENCE
SSF	SUPER SILT FENCE
SCE	STABILIZED CONSTRUCTION ENTRANCE
[ ]	CURB INLET PROTECTION

STANDARD STABILIZATION NOTE

"Following initial soil disturbance or redisturbance, permanent of temporary stabilization shall be completed within (7) days as to the surface of all perimeter controls, dikes, swales, ditches, perimeter slopes, and all slopes greater than 3 horizontal to 1 vertical (3:1) and fourteen days (14) as to all other disturbed or graded areas on the project site.

OWNER'S/DEVELOPER'S CERTIFICATION

I/WE HEREBY CERTIFY THAT ALL CLEARING, GRADING, CONSTRUCTION, AND OR DEVELOPMENT WILL BE DONE PURSUANT TO THIS PLAN AND THAT ANY RESPONSIBLE PERSONNEL INVOLVED IN THE CONSTRUCTION PROJECT WILL HAVE A CERTIFICATE OF ATTENDANCE AT A MARYLAND DEPARTMENT OF THE ENVIRONMENT APPROVED TRAINING PROGRAM FOR THE CONTROL OF SEDIMENT AND EROSION BEFORE BEGINNING THE PROJECT. I HEREBY AUTHORIZE THE RIGHT OF ENTRY FOR PERIODIC ONSITE EVALUATION BY THE STATE OF MARYLAND, DEPARTMENT OF THE ENVIRONMENT, COMPLIANCE INSPECTORS."

SIGNATURE _____ DATE _____

PRINTED NAME AND TITLE _____ REGISTRATION NUMBER _____

DESIGN CERTIFICATION

I HEREBY CERTIFY THAT THIS PLAN HAS BEEN DESIGNED IN ACCORDANCE WITH THE "1994 STANDARDS AND SPECIFICATION FOR SOIL EROSION AND SEDIMENT CONTROL, THE 2000 MARYLAND STORMWATER DESIGN MANUAL, VOLUMES I & II AND THE MARYLAND DEPARTMENT OF THE ENVIRONMENT STORMWATER MANAGEMENT REGULATIONS.

DESIGN ENGINEER SIGNATURE _____ DATE _____

PRINTED NAME _____ REGISTRATION NUMBER _____

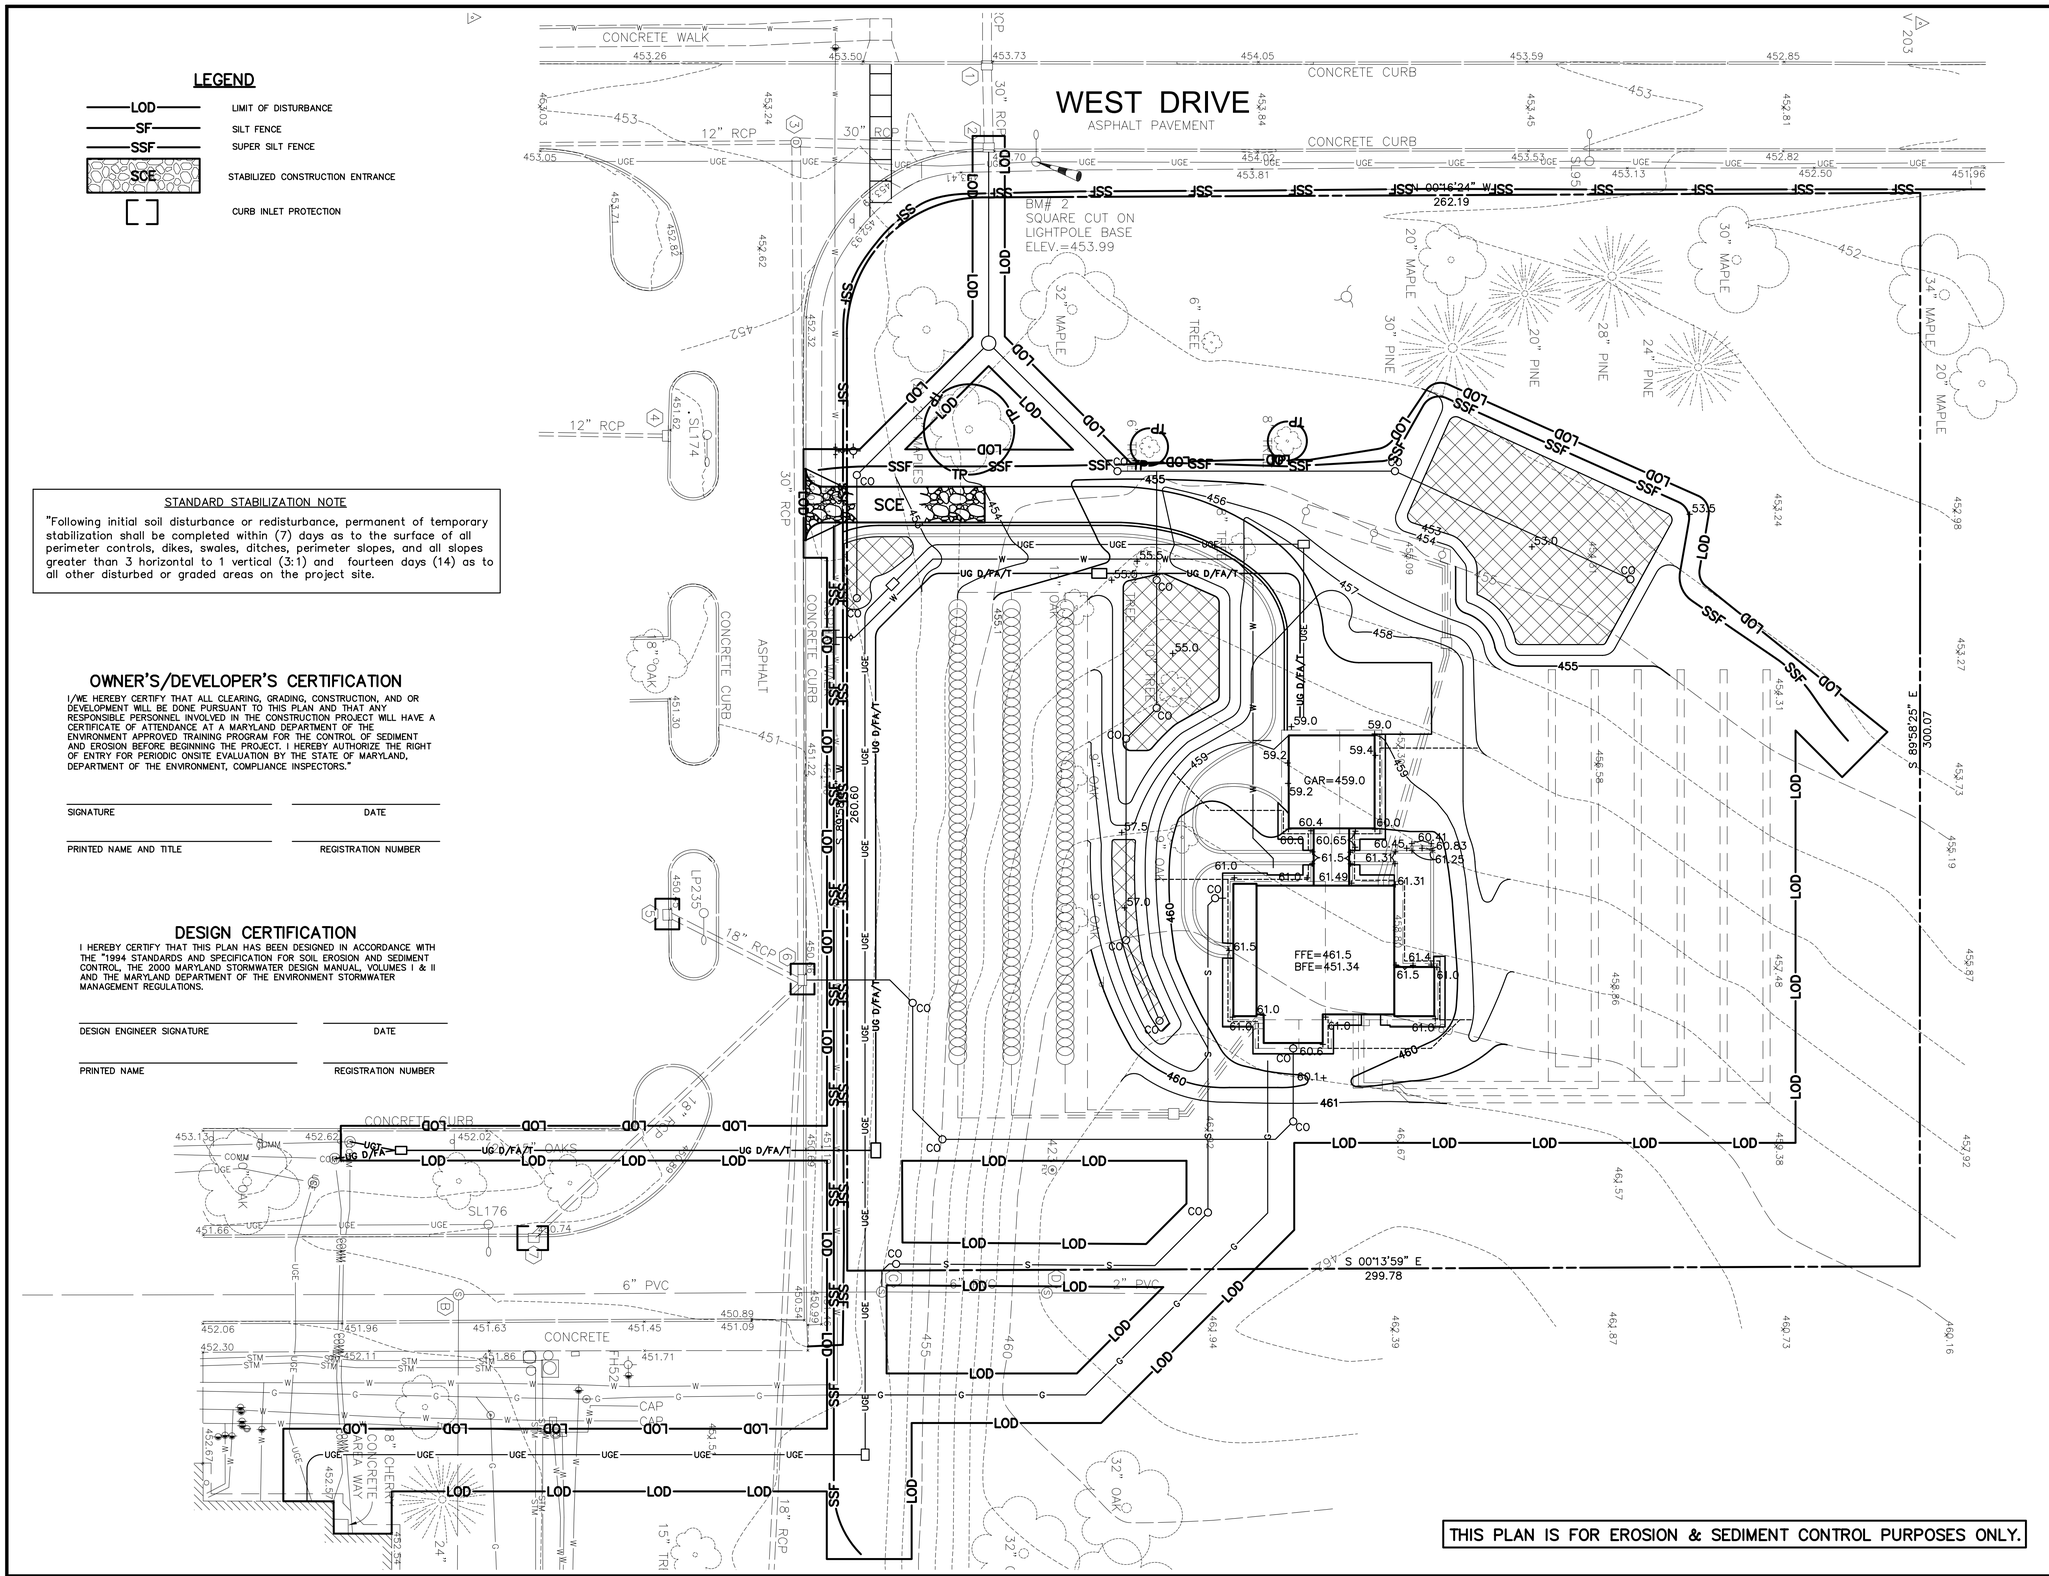

REVISION	DESCRIPTION	BY	DATE
	95% CD SET		01/29/10
	100% CD SET		02/24/10
	ISSUED FOR CONSTRUCTION		03/31/10

PROFESSIONAL CERTIFICATION

"I HEREBY CERTIFY THAT THESE DOCUMENTS WERE PREPARED OR APPROVED BY ME, AND THAT I AM A DULY LICENSED PROFESSIONAL ENGINEER UNDER THE LAWS OF THE STATE OF MARYLAND, LICENSE NO. 12564, EXPIRATION DATE 08/10/2011."

1"=20' 20' 10' 0' 20' 40'

KEAST & HOOD CO.
Structural Engineers
1850 M Street NW Washington, DC 20036
(202) 223-1941 Fax (202) 223-1942

AMT
A. MORTON THOMAS AND ASSOCIATES, INC.
CONSULTING ENGINEERS
12750 TWINBROOK PARKWAY ROCKVILLE, MD 20852
(301) 881-2545 FAX:(301) 881-0814
EMAIL: AMT1@AMTENGINEERING.COM

NIST NORTH

FOR OFFICIAL USE ONLY

U.S. DEPARTMENT OF COMMERCE
NATIONAL INSTITUTE OF STANDARDS AND TECHNOLOGY
PLANT DIVISION

NET ZERO ENERGY RESIDENTIAL TEST FACILITY

EROSION & SEDIMENT CONTROL PLAN

SH.NO. ____ OF ____ DWG. C-401

APPROVED BY	DATE	SPONSOR	DATE	MAINTENANCE ENG. OFF.	DATE	FIRE PROTECTION SVS.	DATE	S.H. & E. DIV.	DATE	FACILITIES ENGR. OFF.	DATE	PROJECT LEADER	DATE	KS/DN DRAWN BY	02/01/10 DATE	SB134109CQ0026/69331 PROJECT/W.O.	DESIGN PROJ. #